


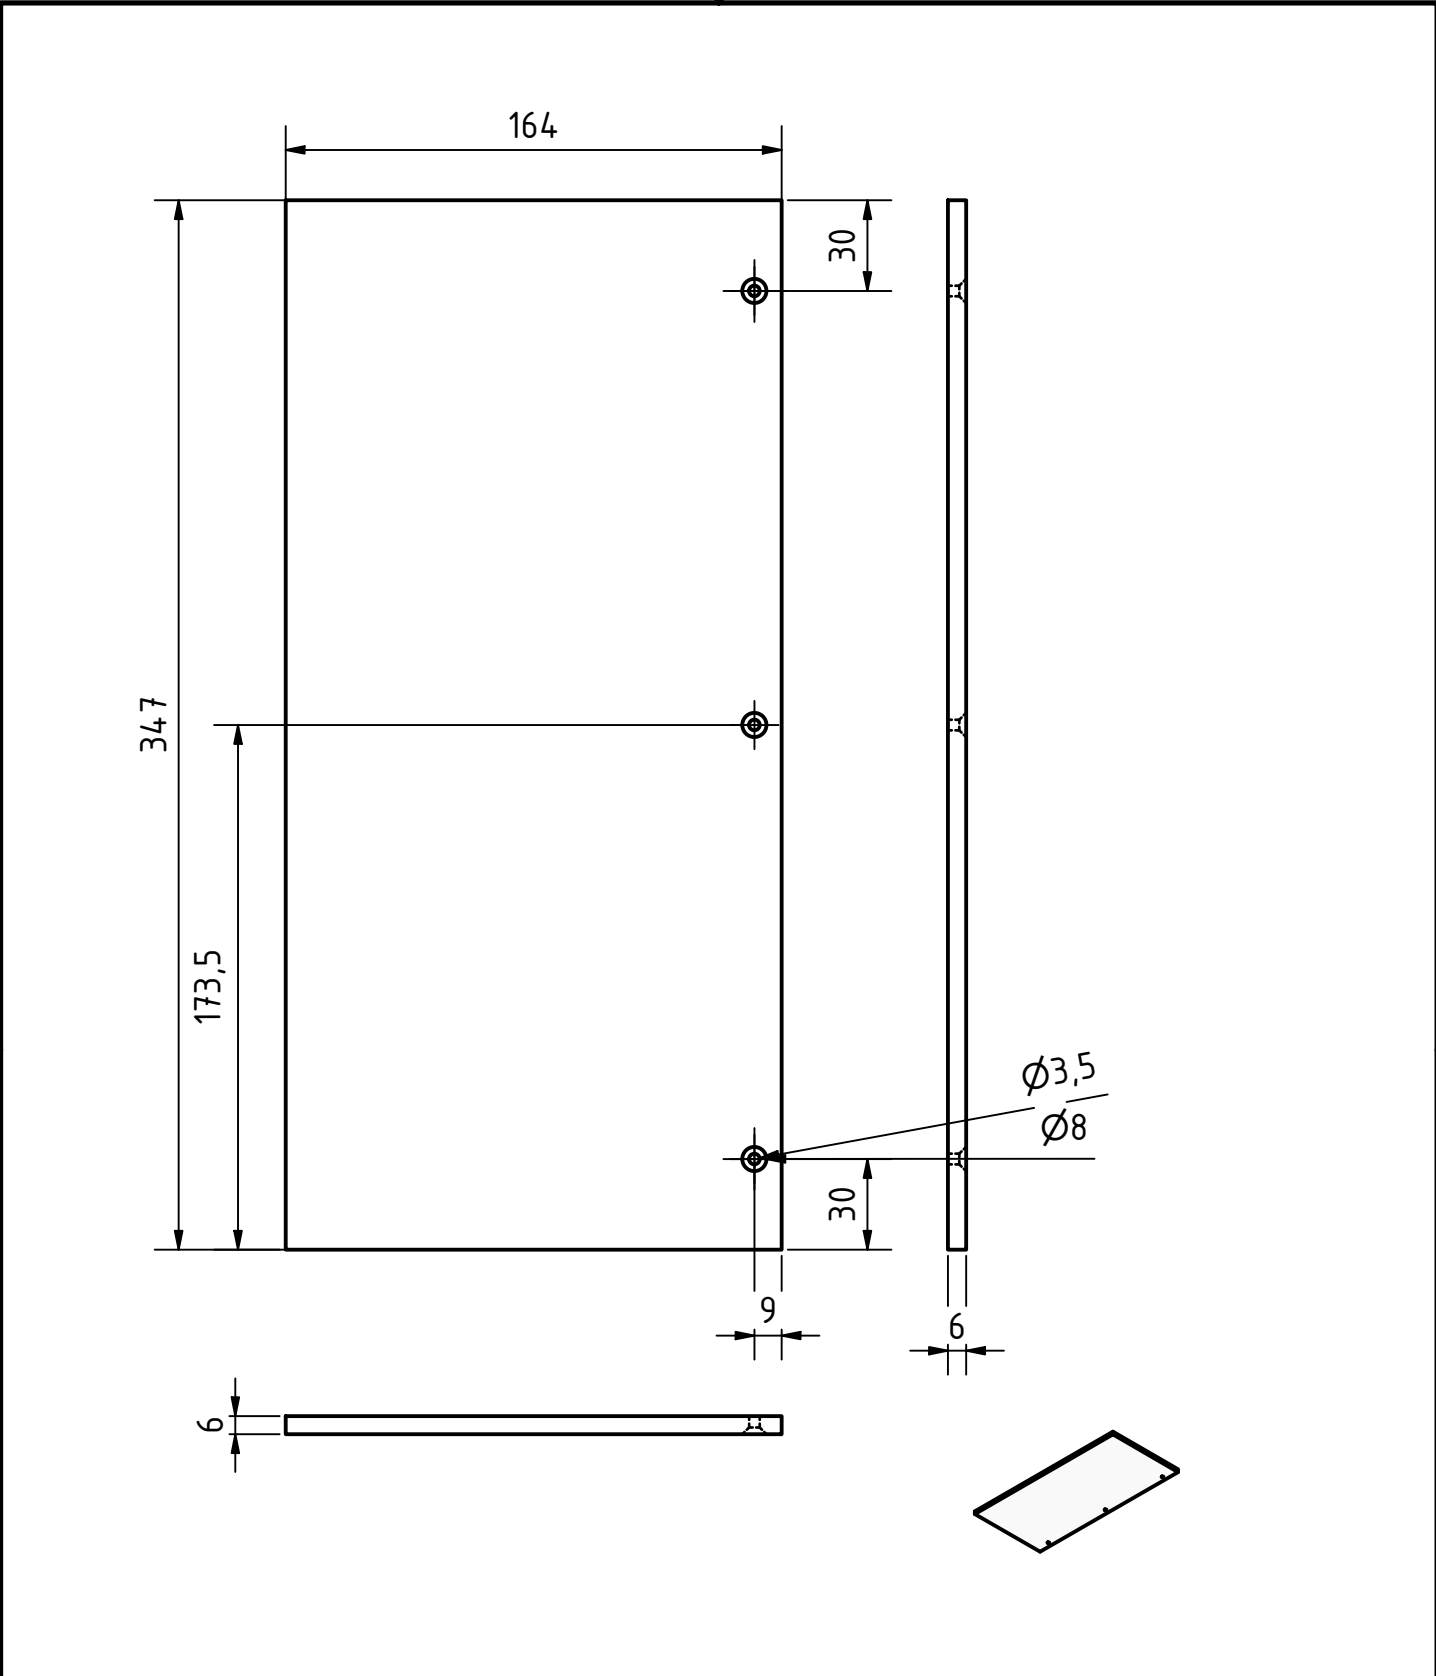

					Date	Name	Side wall		
				Drawn	07/09/2026	SK/DK			
				Checked		SK/DK			
				Standard					
							Side wall		
							1		
							A4		
State	Changes	Date	Name						